


Fração F | Piso 0 | Armaduras inferiores

Prancha original com identificadores adicionados. Cada ID aponta para uma chamada de armadura, não para uma barra isolada.

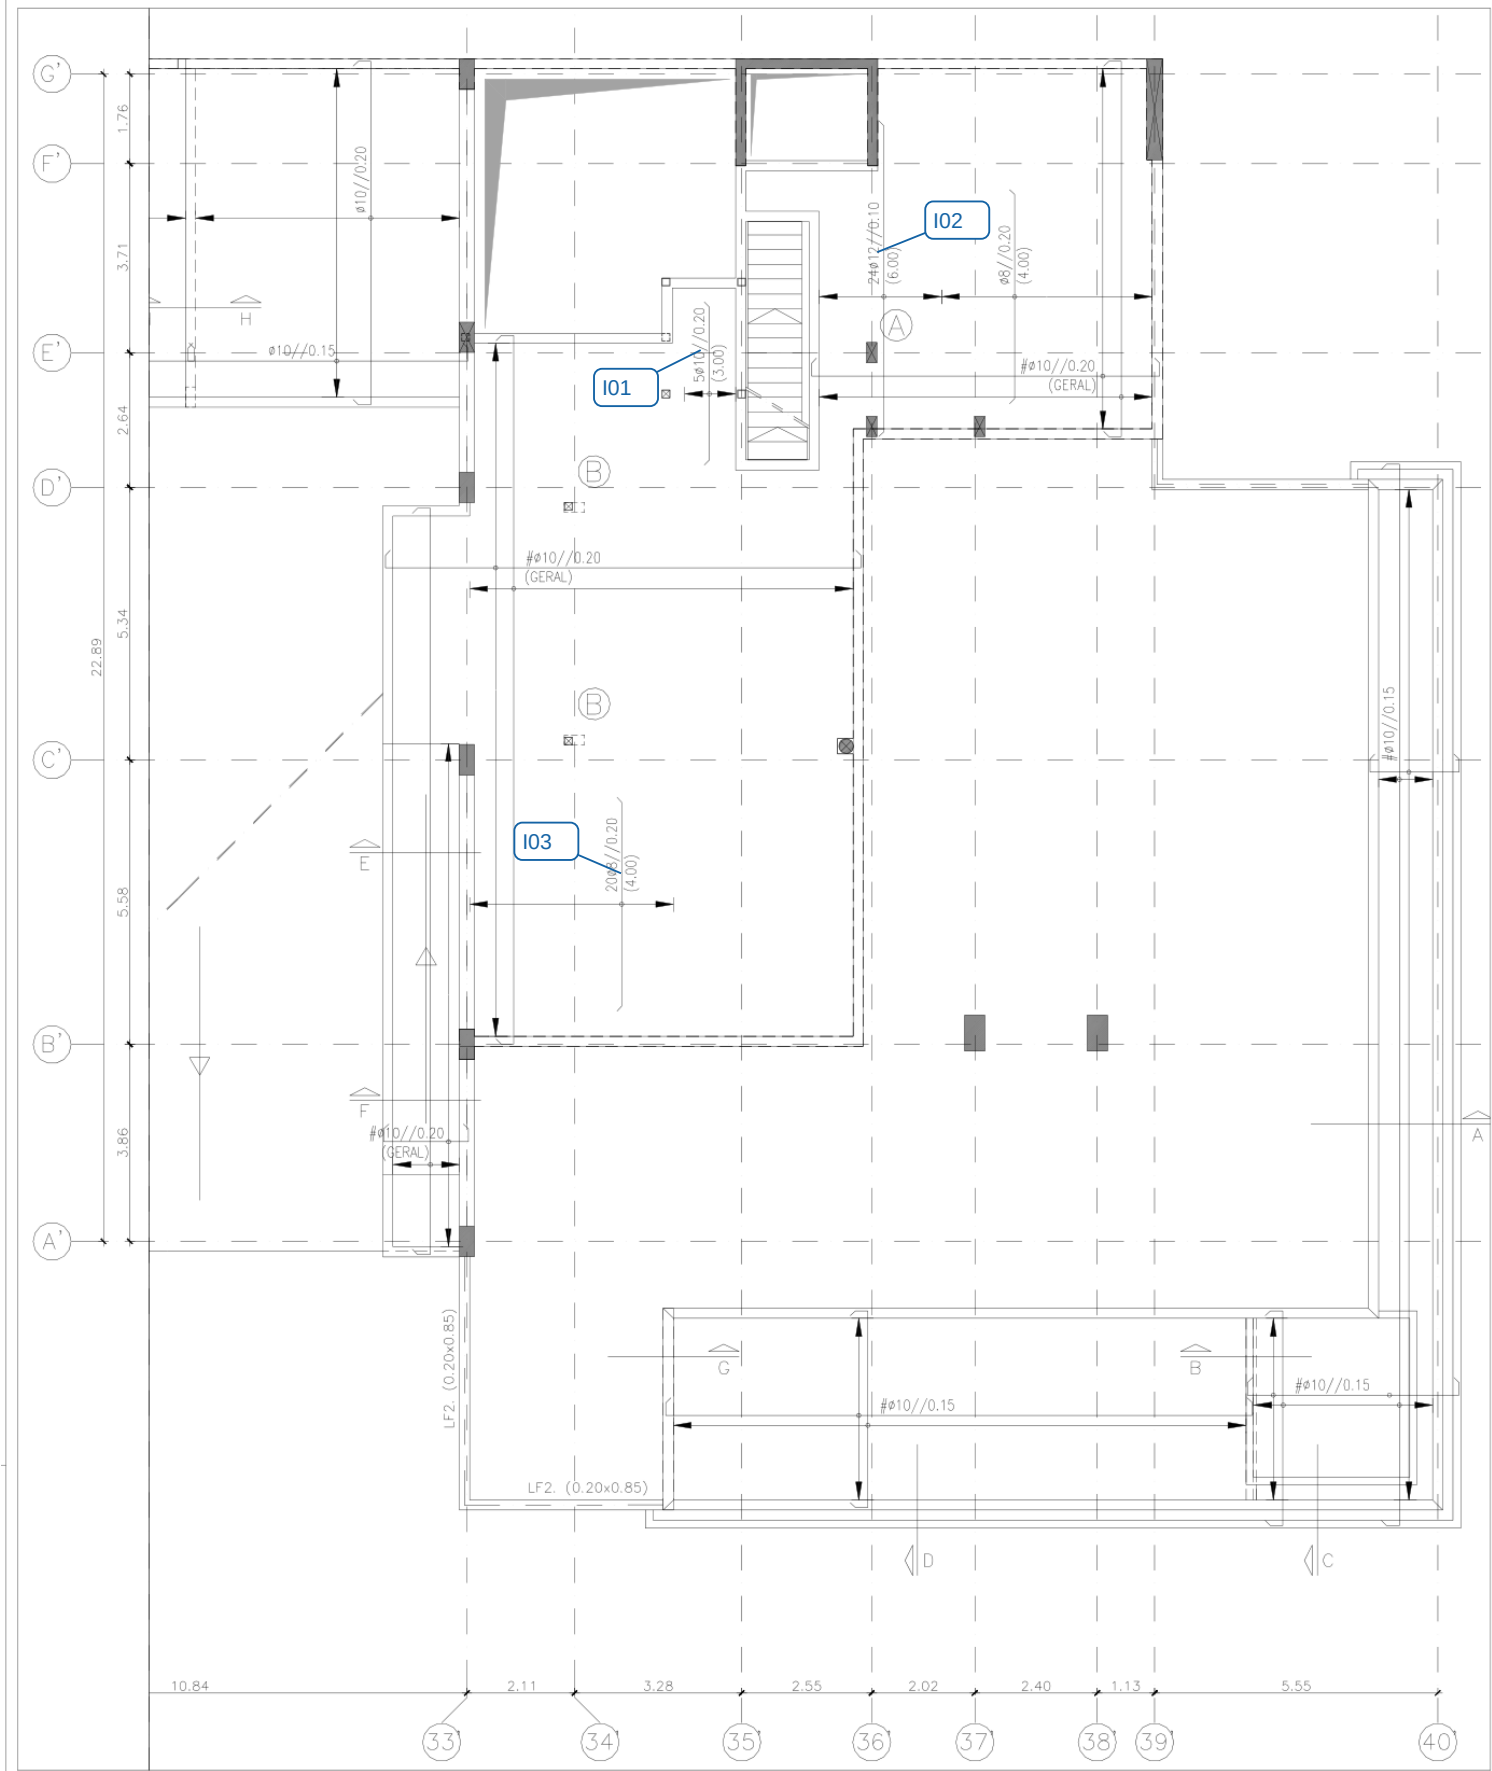

Quantidade e cálculo por chamada


ID	n	Ø mm	L/barra m	n × L = metros	Peso kg	
I01	5	10	3,00		15,00	9,26
I02	24	12	6,00		144,00	127,87
I03	20	8	4,00		80,00	31,60

SUBTOTAL DAS 3 CHAMADAS: 168,73 kg

Cálculo: n × comprimento indicado × peso por metro.
Pesos: Ø8 = 0,395; Ø10 = 0,617; Ø12 = 0,888 kg/m.
Comprimentos usados tal como indicados entre parênteses.
Malhas gerais e chamadas sem n explícito: PENDENTE.
Comprimentos adicionais nas bandas: conferir nota do projeto.
Não foram somadas ancoragens extra a estas parcelas.

Fração F | Piso 0 | Armaduras superiores

Prancha original com identificadores adicionados. Cada ID aponta para uma chamada de armadura, não para uma barra isolada.

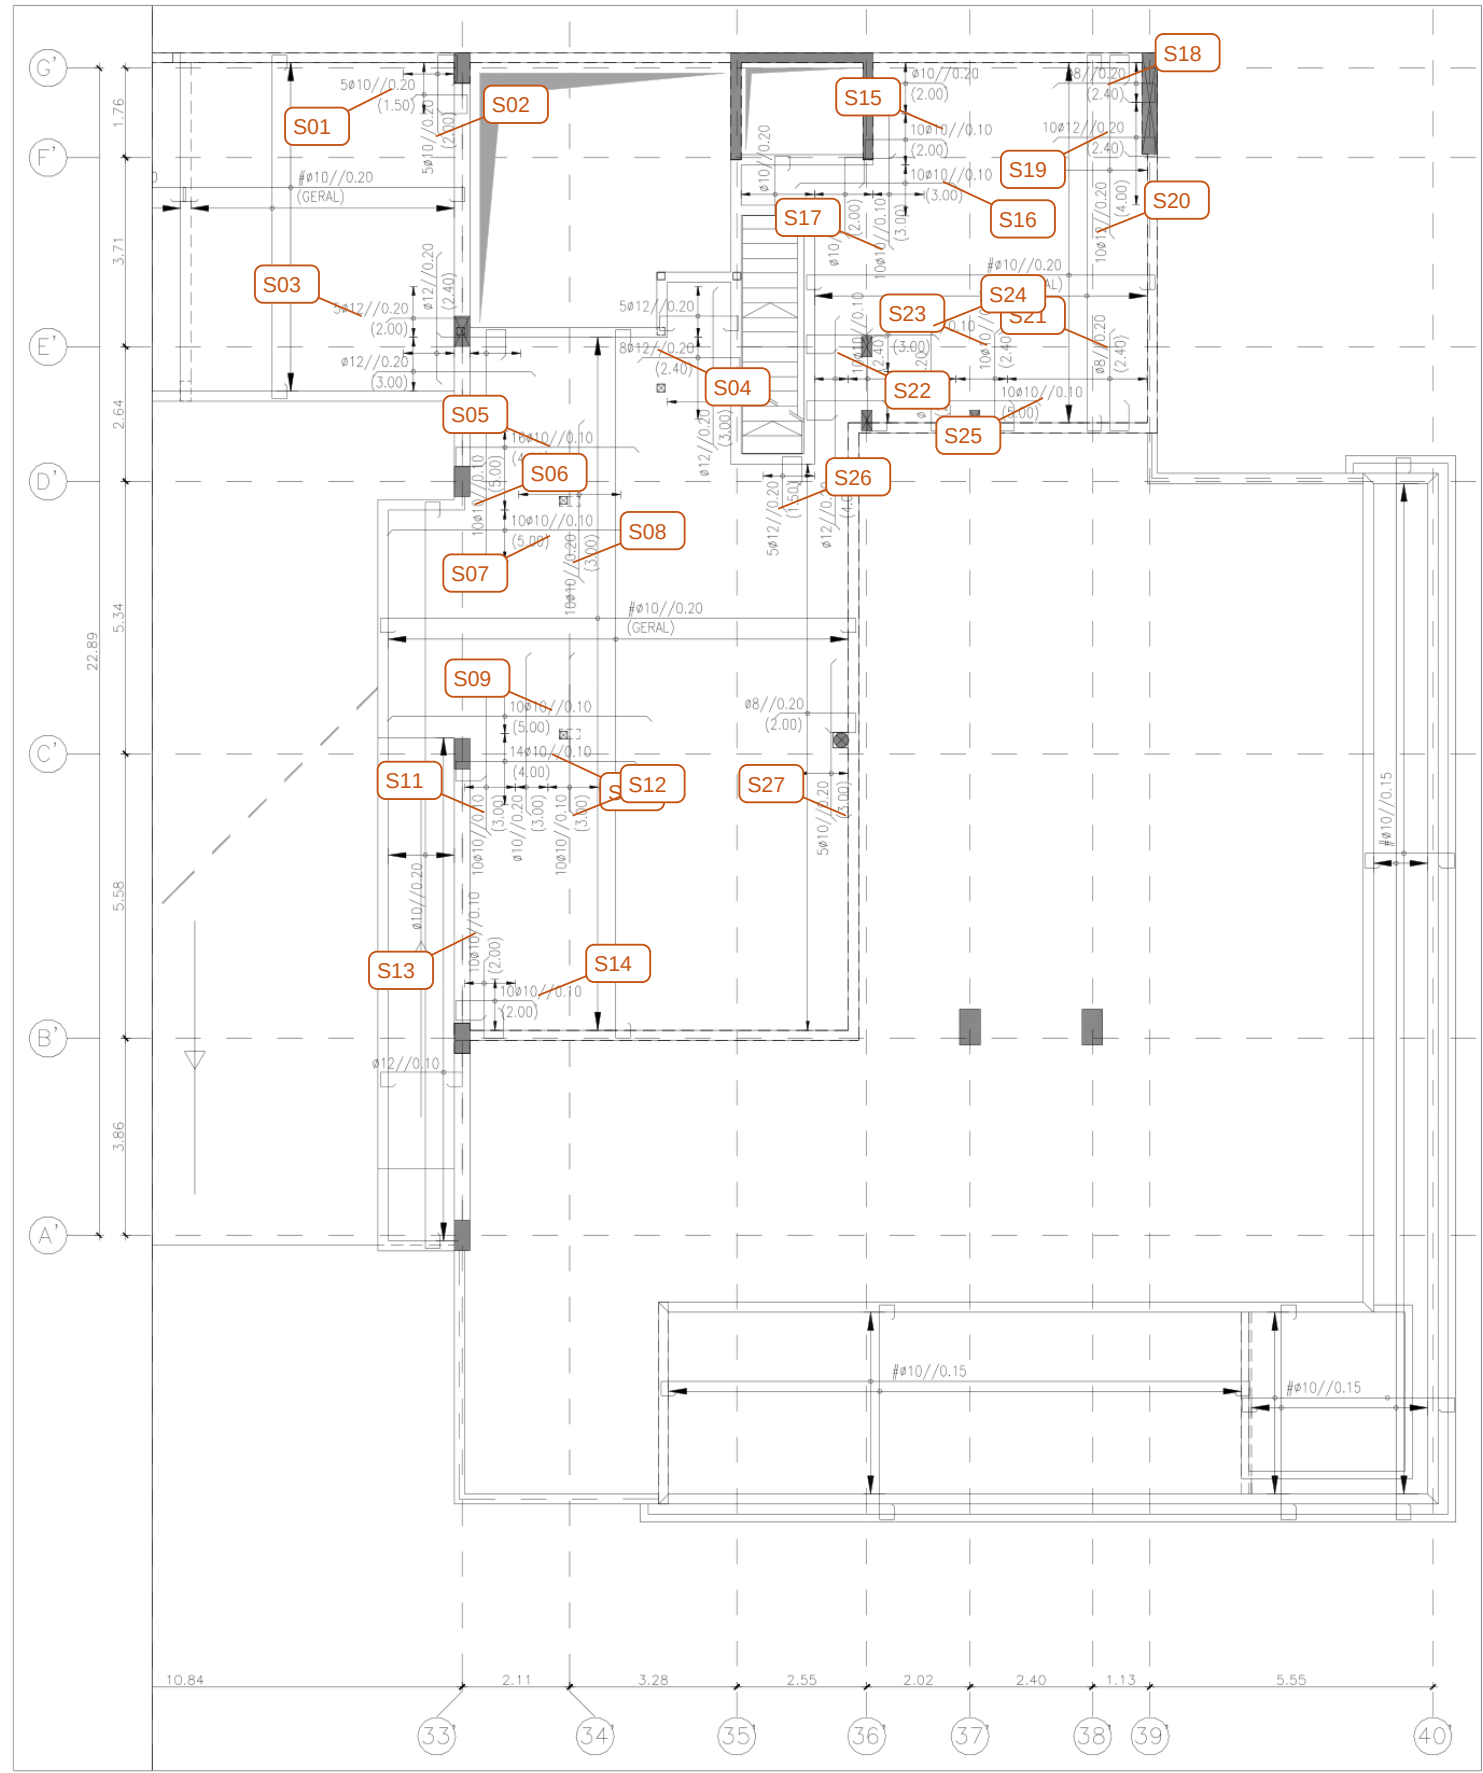

Quantidade e cálculo por chamada

ID	n	Ø mm	L/barra m	n × L = metros	Peso kg	
S01	5	10	1,50	7,50	4,63	
S02	5	10	2,00	10,00	6,17	
S03	5	12	2,00	10,00	8,88	
S04	8	12	2,40	19,20	17,05	
S05	16	10	4,00	64,00	39,49	
S06	10	10	5,00	50,00	30,85	
S07	10	10	5,00	50,00	30,85	
S08	10	10	3,00	30,00	18,51	
S09	10	10	5,00	50,00	30,85	
S10	14	10	4,00	56,00	34,55	
S11	10	10	3,00	30,00	18,51	
S12	10	10	3,00	30,00	18,51	
S13	10	10	2,00	20,00	12,34	
S14	10	10	2,00	20,00	12,34	
S15	10	10	2,00	20,00	12,34	
S16	10	10	3,00	30,00	18,51	
S17	10	10	3,00	30,00	18,51	
S18	8	10	2,40	19,20	11,85	
S19	10	12	2,40	24,00	21,31	
S20	10	12	4,00	40,00	35,52	
S21	8	10	2,40	19,20	11,85	
S22	10	10	2,40	24,00	14,81	
S23	10	10	2,40	24,00	14,81	
S24	10	10	3,00	30,00	18,51	
S25	10	10	5,00	50,00	30,85	
S26	5	12	1,50	7,50	6,66	
S27	5	10	3,00	15,00	9,26	

SUBTOTAL DAS 27 CHAMADAS: 508,30 kg

Cálculo: n × comprimento indicado × peso por metro.
Pesos: Ø8 = 0,395; Ø10 = 0,617; Ø12 = 0,888 kg/m.
Comprimentos usados tal como indicados entre parênteses.
Malhas gerais e chamadas sem n explícito: PENDENTE.
A nota superior já inclui 60Ø nas amarrações retas e 50Ø nos ferros de bordo. Não somar novamente.

Memória de cálculo e limites do levantamento

Quantidades identificadas na prancha 42; parcelas separadas do total ainda por apurar.

1. Exemplo I02: 24 varões Ø12, comprimento indicado 6,00 m.

Comprimento: $24 \times 6,00 = 144,00$ m. Peso: $144,00 \times 0,888 = 127,872$ kg.

2. Exemplo I03: 20 varões Ø8, comprimento indicado 4,00 m.

Comprimento: $20 \times 4,00 = 80,00$ m. Peso: $80,00 \times 0,395 = 31,600$ kg.

3. Exemplo S05: 16 varões Ø10, comprimento indicado 4,00 m.

Comprimento: $16 \times 4,00 = 64,00$ m. Peso: $64,00 \times 0,617 = 39,488$ kg.

Resumo das chamadas com n e comprimento explícitos

Ø8: 20 varões | 80,00 m | 31,60 kg

Ø10: 216 varões | 693,90 m | 428,14 kg

Ø12: 62 varões | 244,70 m | 217,29 kg

Subtotal parcial: 677,03 kg. TOTAL DA LAJE: PENDENTE.

Falta quantificar:

- Malhas gerais Ø10/0,20 e Ø10/0,15: limites líquidos, direções e comprimentos de corte.
- Chamadas que indicam diâmetro/espacamento sem quantidade explícita, incluindo reforços Ø8 e Ø12.
- Bordos, secções A-H, LF2, singularidades e interfaces: evitar omissões e dupla contagem.
- Prolongamentos indicados nas notas inferiores, quando aplicáveis; não acrescentados por estimativa.

Para malhas: contar os varões pelas posições inicial/final e espaçamento de cada zona.

O número não pode ser obtido apenas dividindo a área da laje pelo espaçamento.

As peças cortadas junto da escada e mudanças de contorno exigem comprimentos próprios.

Os IDs I01-I03 e S01-S27 foram criados neste levantamento; não são marcas originais do projetista.

Os pesos são teóricos com a mesma tabela arredondada usada na planilha, sem perdas de compra.